



All dimensions and levels are from top of ramp
(FFL+30mm/SSL+45mm) including HSK and HSG

Well Head 1:25

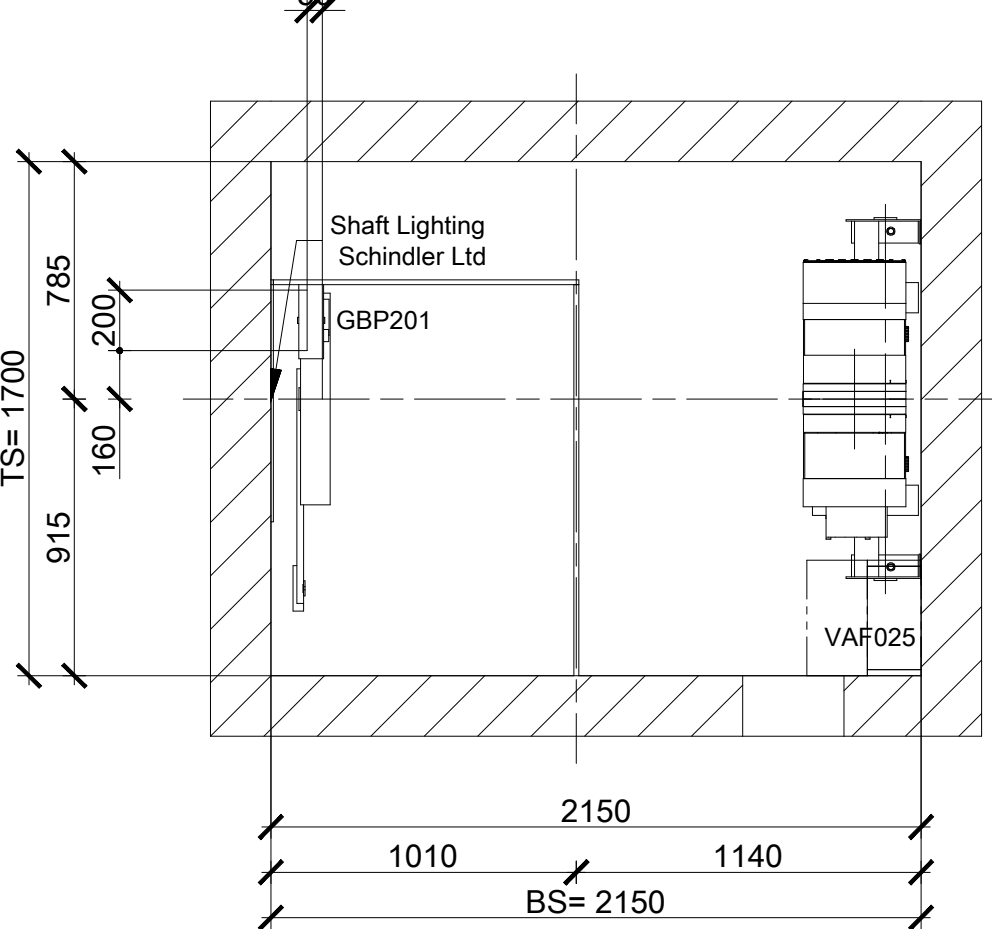


Door Detail 1:20

Entrance: 6 Control box Position right (NEXT_R)

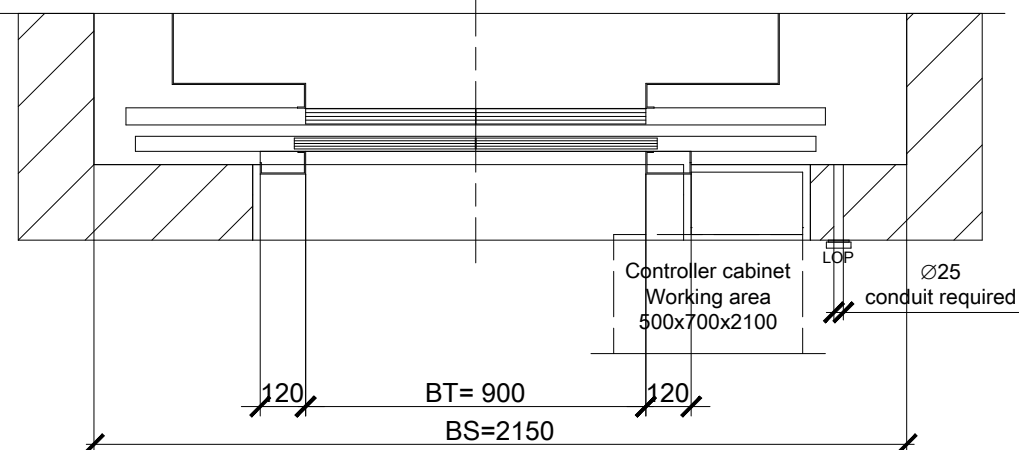


Acc code: Electric lighting (with switch) shall provide at least 200 lux at working areas. The internal lamp in the cabinet assures the required 200 lux at the working area in front of control box/LDU

Well 1:20

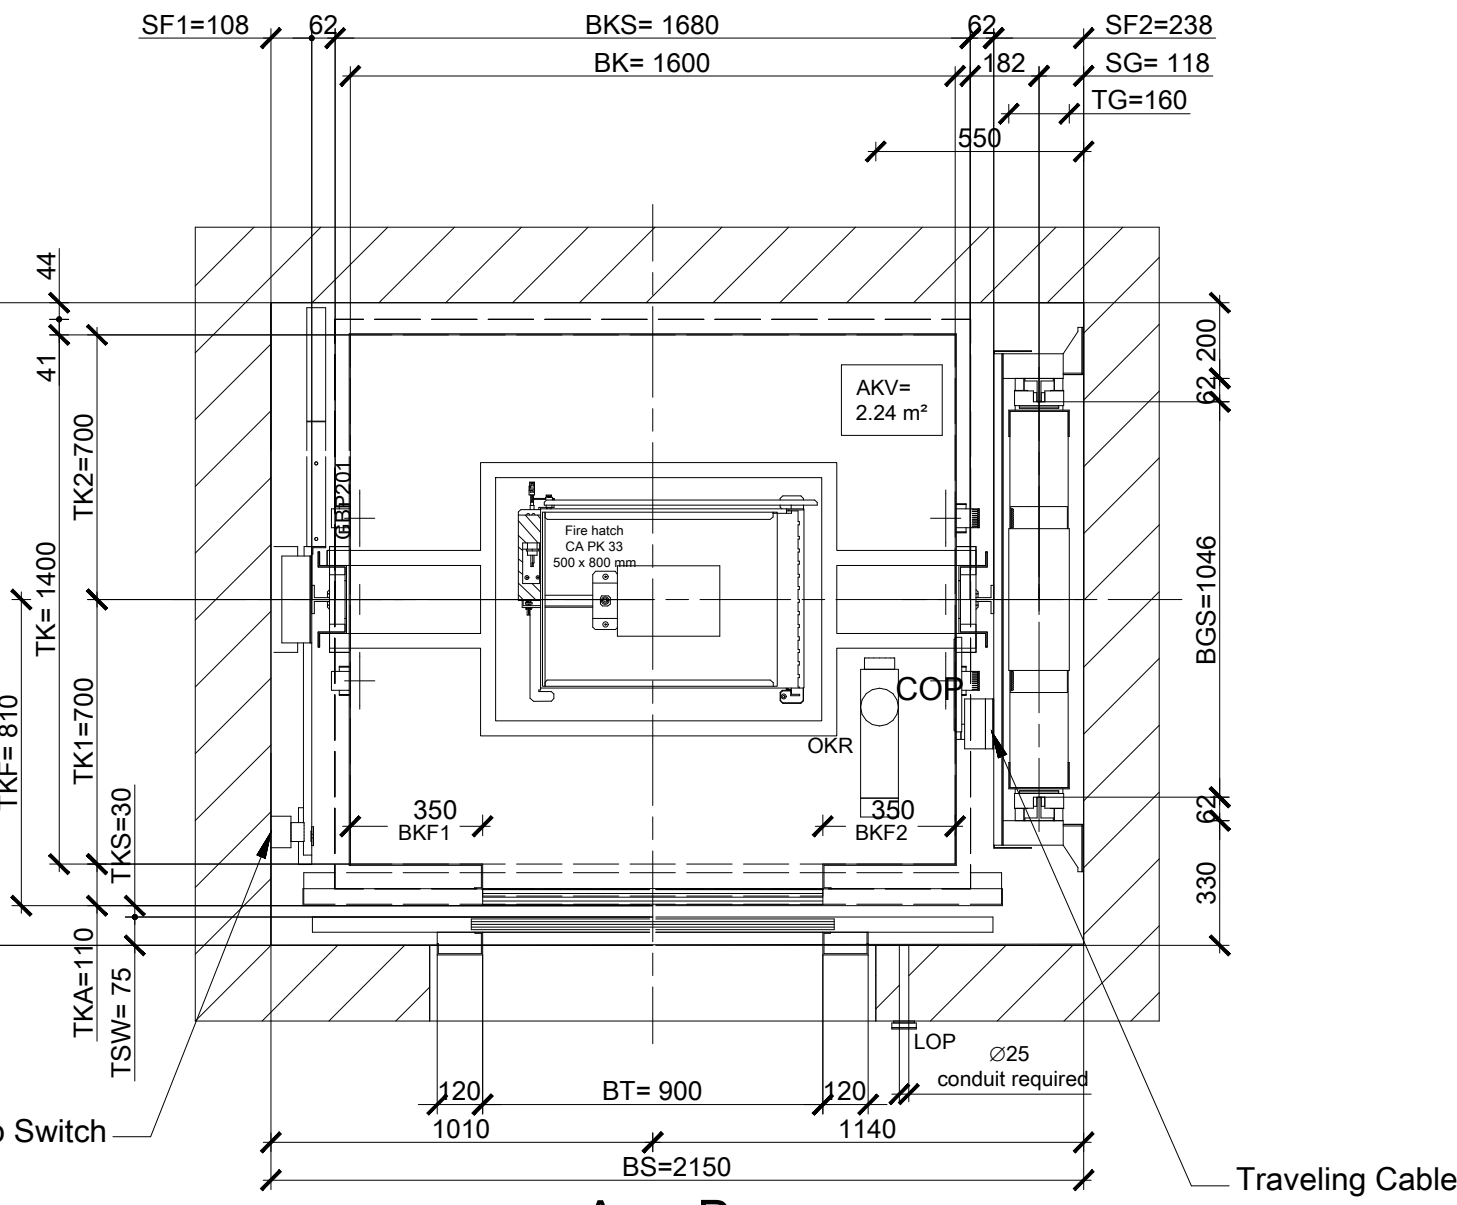


Access: 0, 1, 2, 3, 4, 5

Overview of refuge space situation In hoistway pit

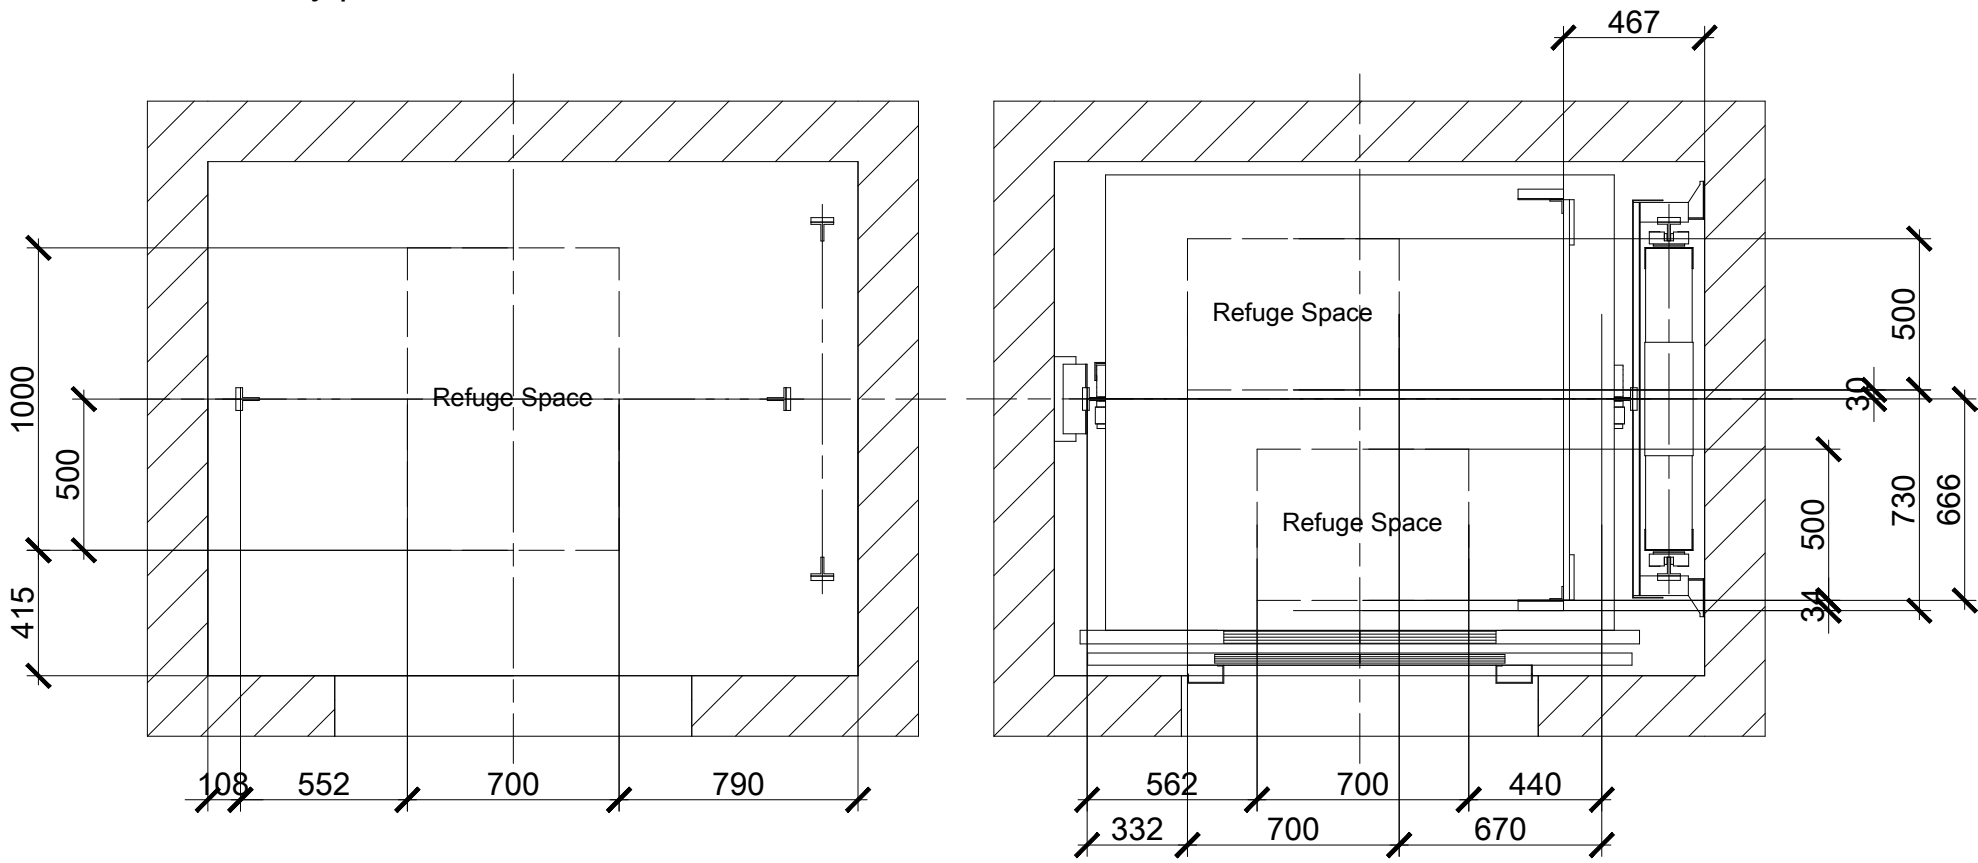


Access side 1 1:50

Entrance: 0 Main stop

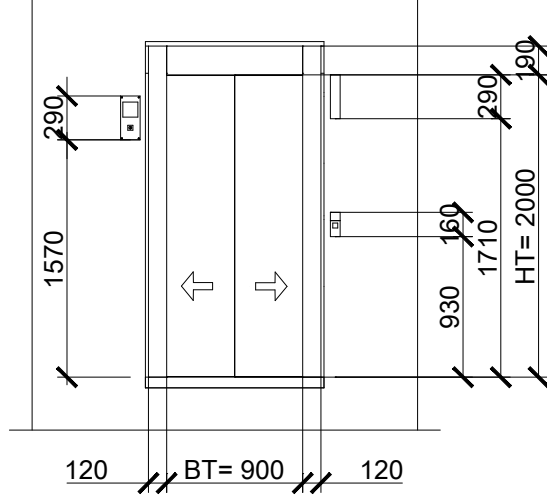


Access side 1 1:50

Entrance: All remaining floors

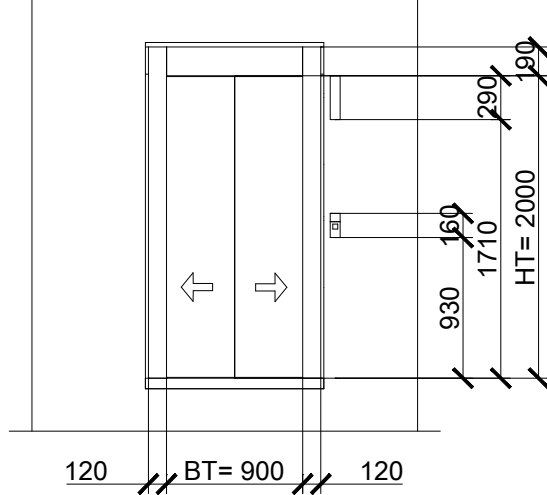


Access side 1 1:50


Entrance: 6 Control box (Position left (NEXT_L))

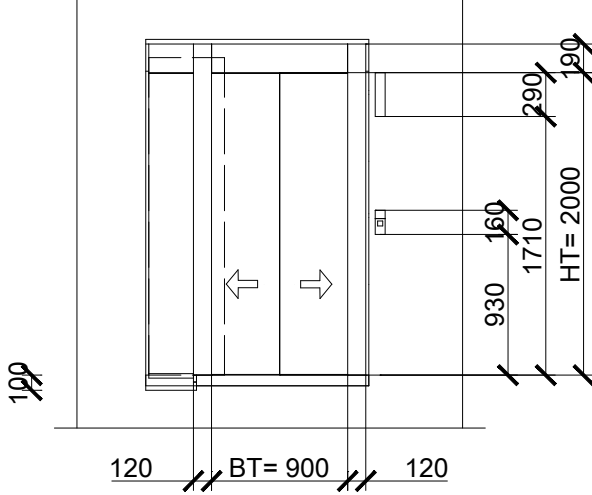

Section B-B 1:75

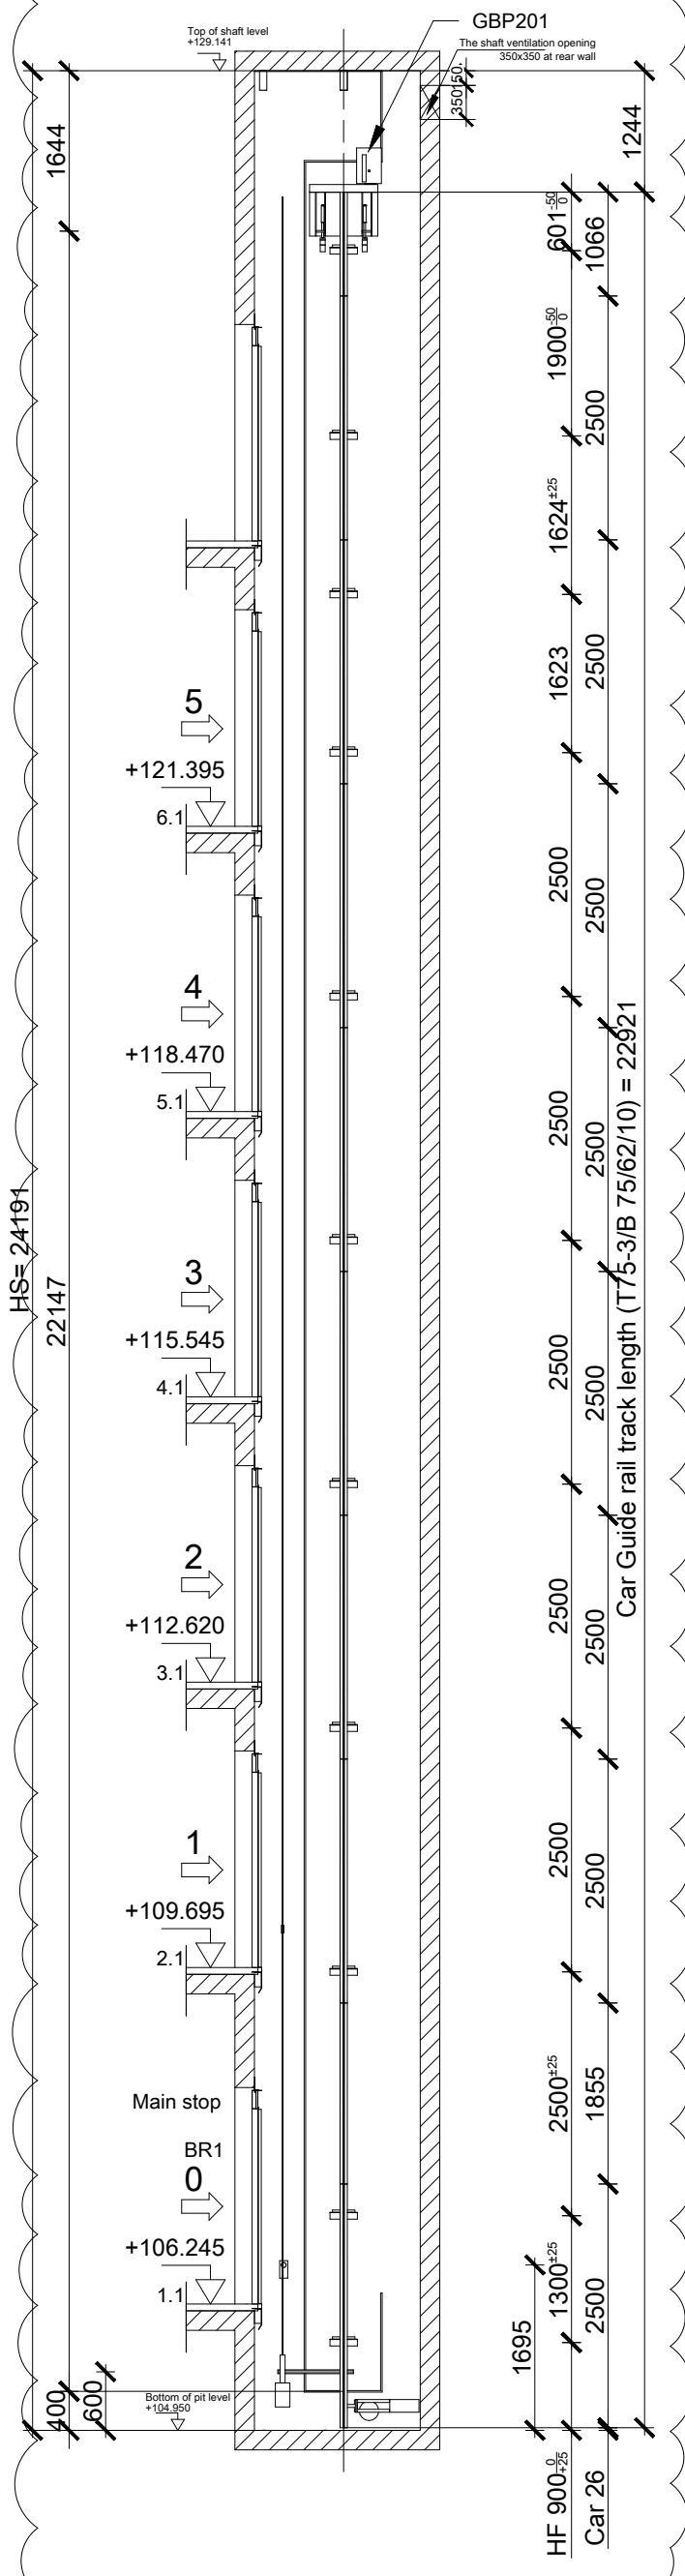


Section A-A 1:75

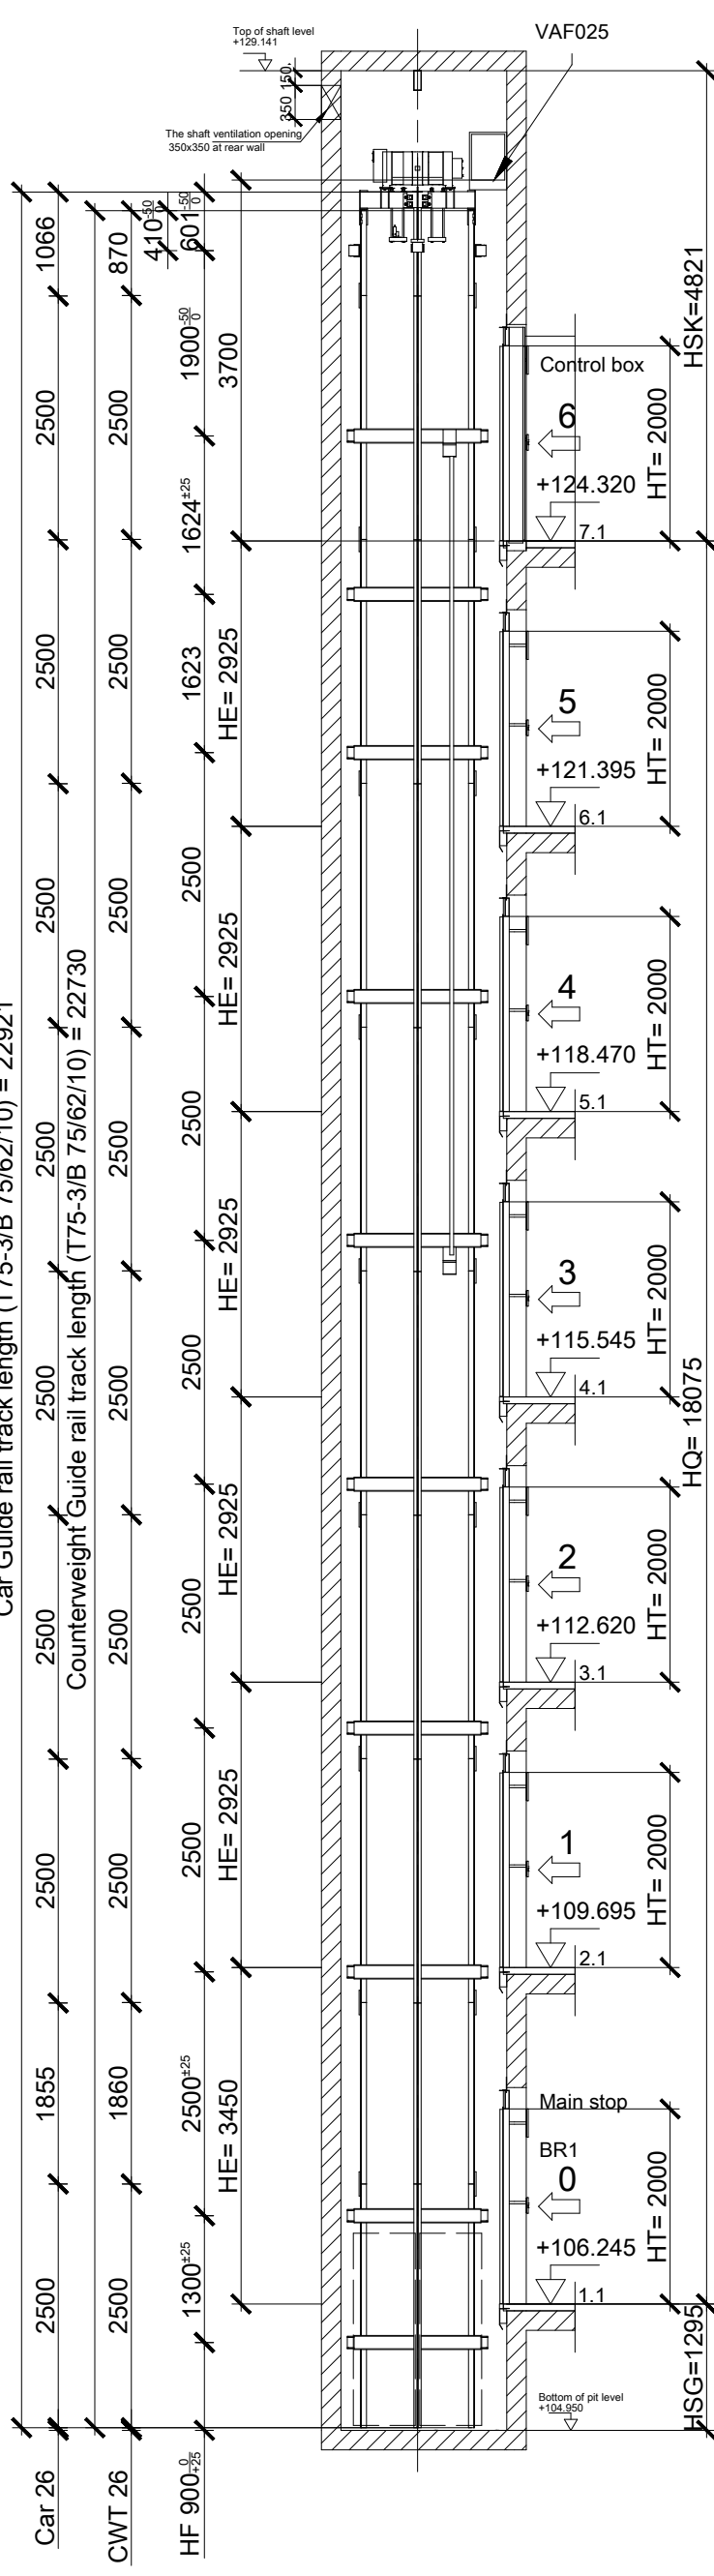


Wellhead and Wellpit 1:75


Section B-B (H0.6x)

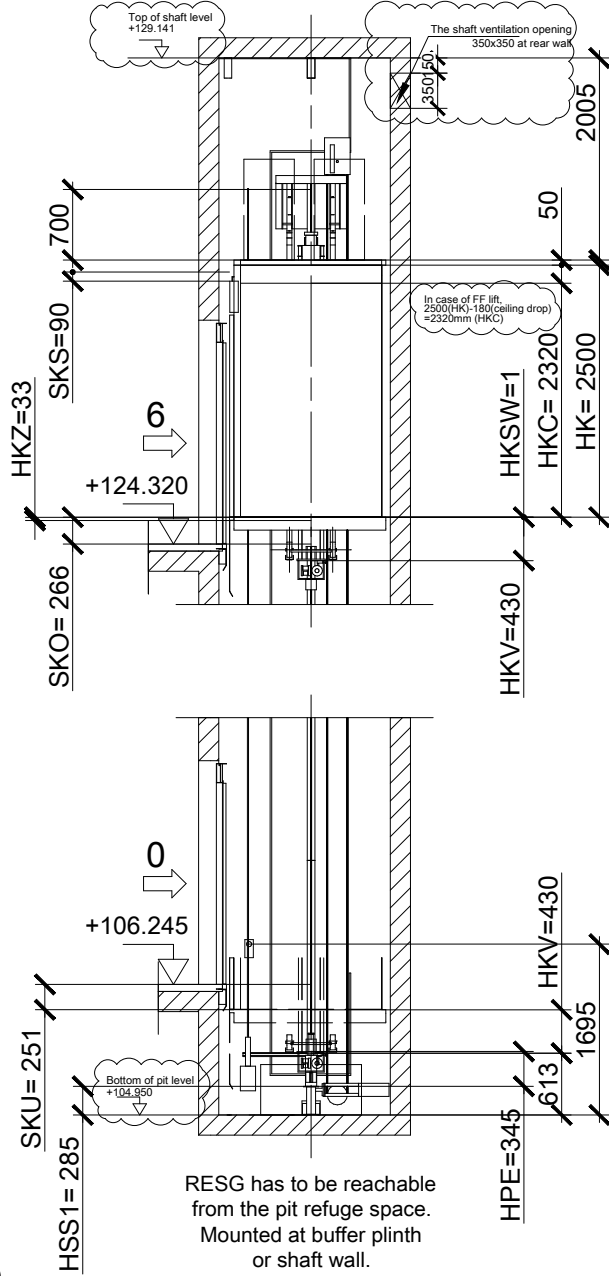


Section A-A (H0.6x)

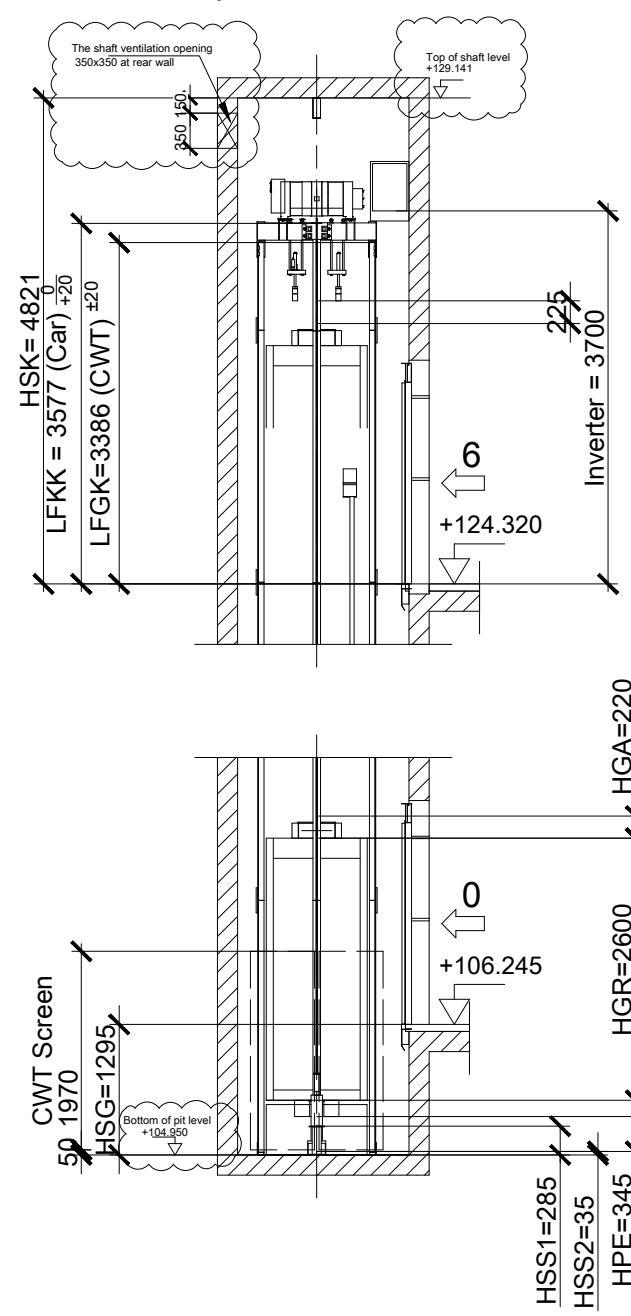

Car position at bottom floor

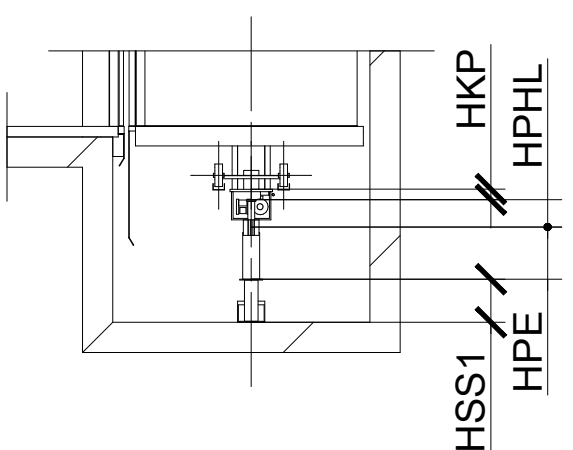

Car position at top floor

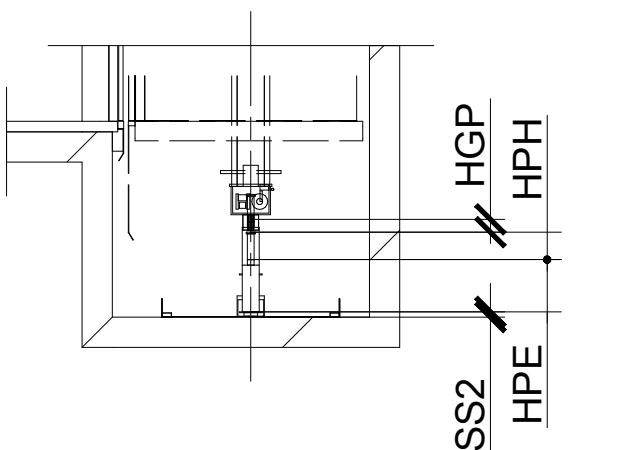

	Car buffer	Counterweight buffer
	MLB16	MLB16
(HP) [mm]	526	526
HPH/HPHL[mm]	174.3 / 181	174.3 / 181
HKP/HGP [mm]	70 -5/0	85 -20/0
HSS1/2 [mm]	285	35
HPE [mm]	345	345
Quantity	2	1

Refuge spaces

Position and dimension	Label
On car ceiling 700x500x1000 700x500x1000	
In hoistway pit 700x1000x500	

Bracket Selection

HFmax 2800 [mm]	Car side	Counterweight side
Complete hoistway	11 x Z-AL16	1 x L-B L 160/190 1
Type of clip for guide rail fixation	SL3 (SHORT)	SL2

A - Construction


Revision	Modification	Modified by	Reviewed by	Date
P01	First issue (CP 361)	ABOOHAAN	HOOLEWI	28/08/2025
P02	Change pit depth, Lift function to passenger	BENAVUE	HOOLEWI	09/03/2026
C01	Issued to Construction	ABOOHAAN	HOOLEWI	11/06/2026

Installation - Block F - L3 FF

Product Line:

Schindler 6000

Building	Stoneyard, Birmingham - Phase 1
Sales Unit Name	Block F - L3 FF
Address	High Street - B9 4LS Birmingham
Client	Caddick Construction Limited - Temple Street 31 - B2 5DB Birmingham

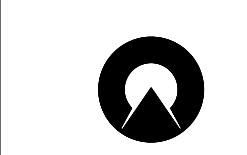

Schindler Ltd
400 Daswood Lang Road
Bourne Business Park
KT15 2HJ Addlestone

Contact: Mr. Keith Docherty

Further inquiries concerning this plan on
Mr. Keith Docherty Tel:

Drawn	ABOOHAAN	28/08/2025	Page
Released	KEITH	28/08/2025	2/6

Comm. No. UKC0011915007

Plan No. SY1-SCH-BF-ZZ-DR-X-01001

This design and information is intellectual property.
It must neither be copied in any way nor used for
manufacturing nor communicated to third parties
without our written consent.

Cette documentation est notre propriété intellectuelle. Sans notre
autorisation écrite, il ne peut être ni copié d'une manière
quelconque ni être utilisé pour la fabrication ni non plus
être communiqué à des tiers.

This design and information is intellectual property.
It must neither be copied in any way nor used for
manufacturing nor communicated to third parties
without our written consent.

