

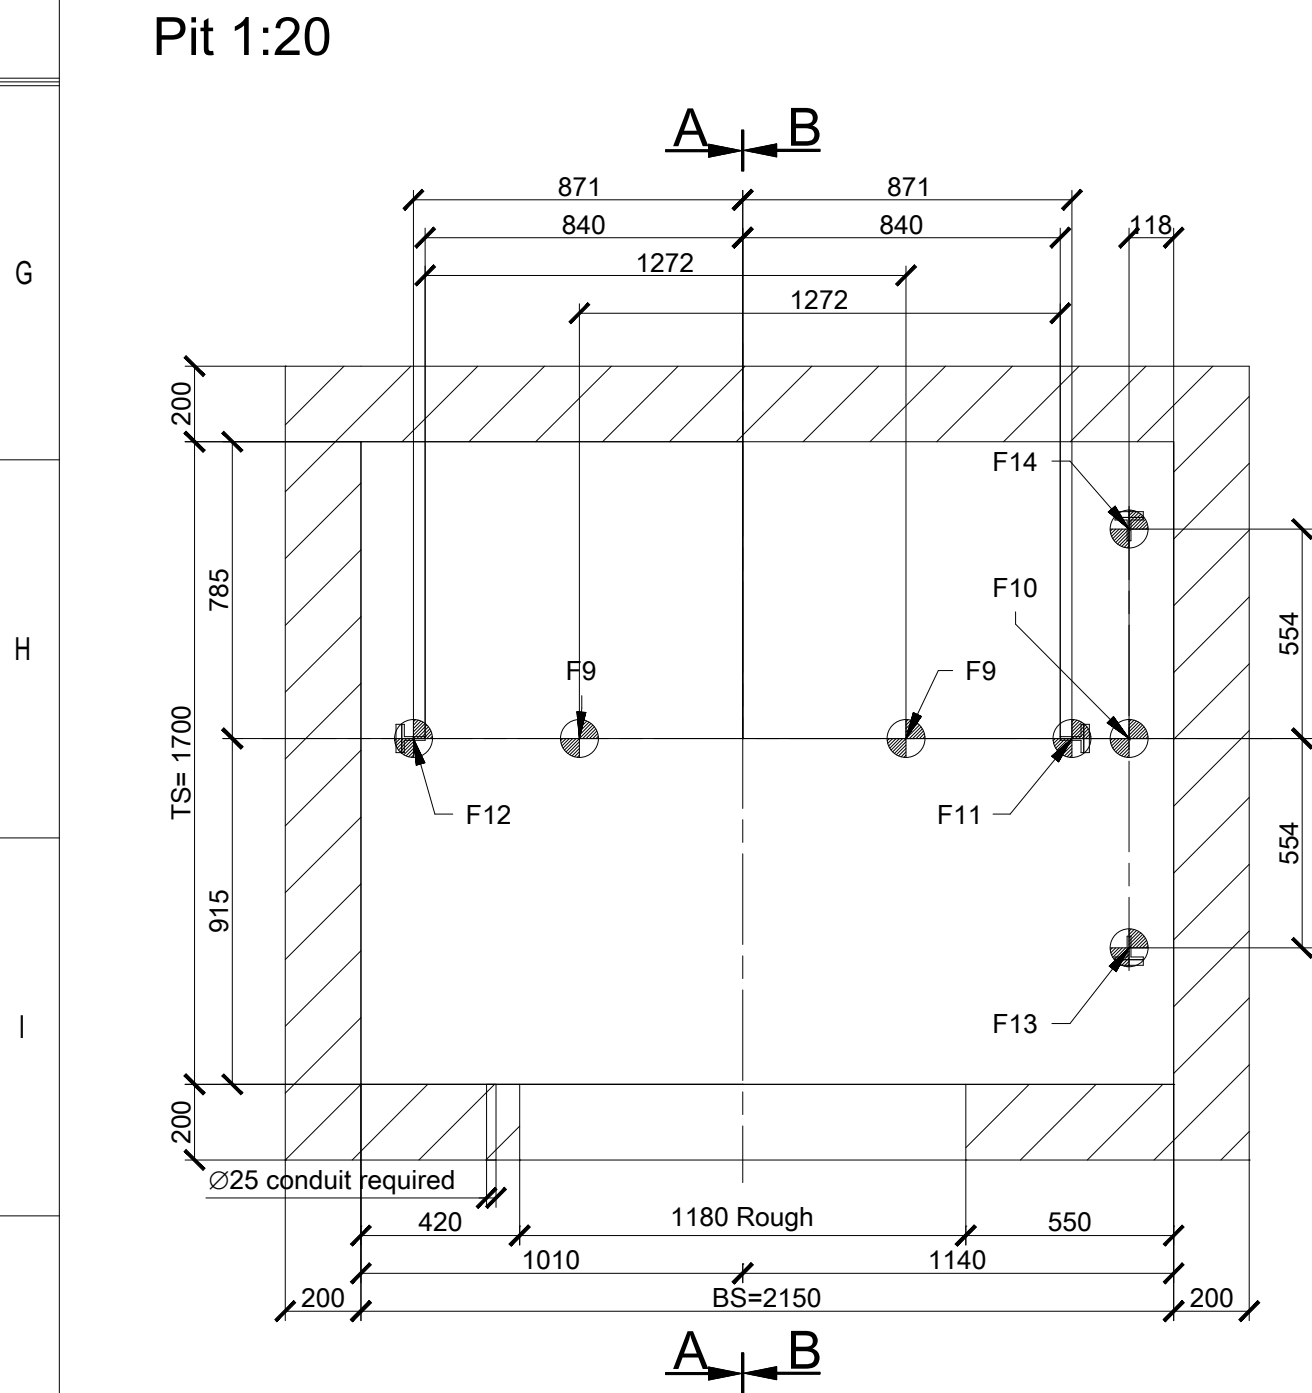
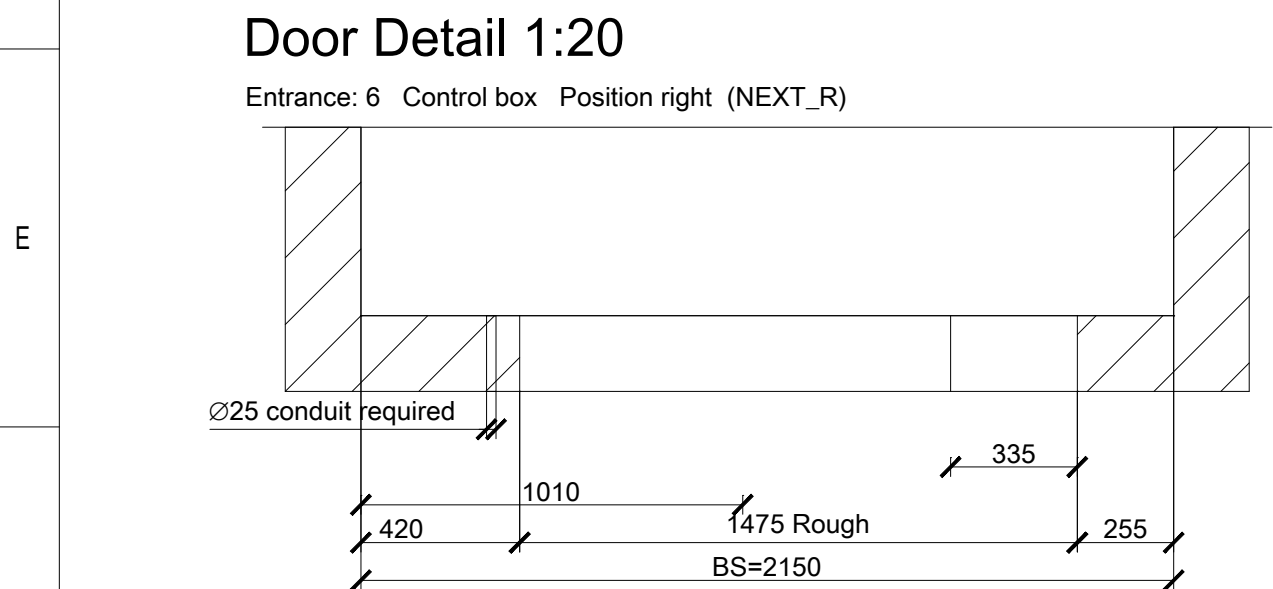
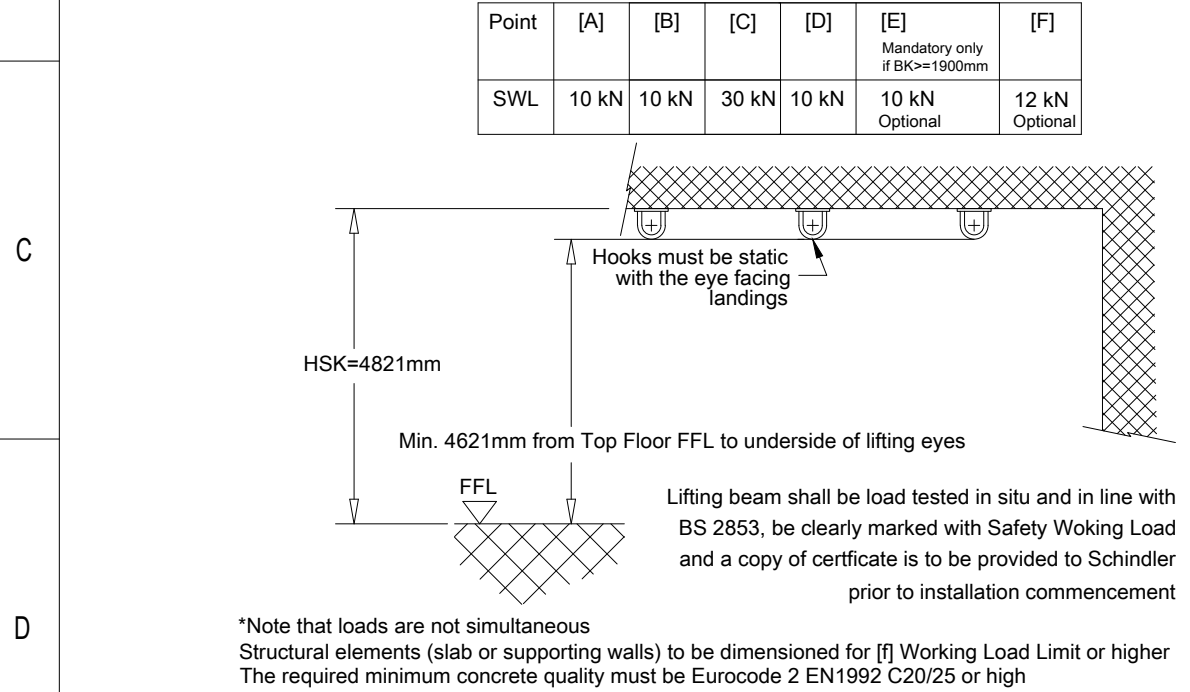
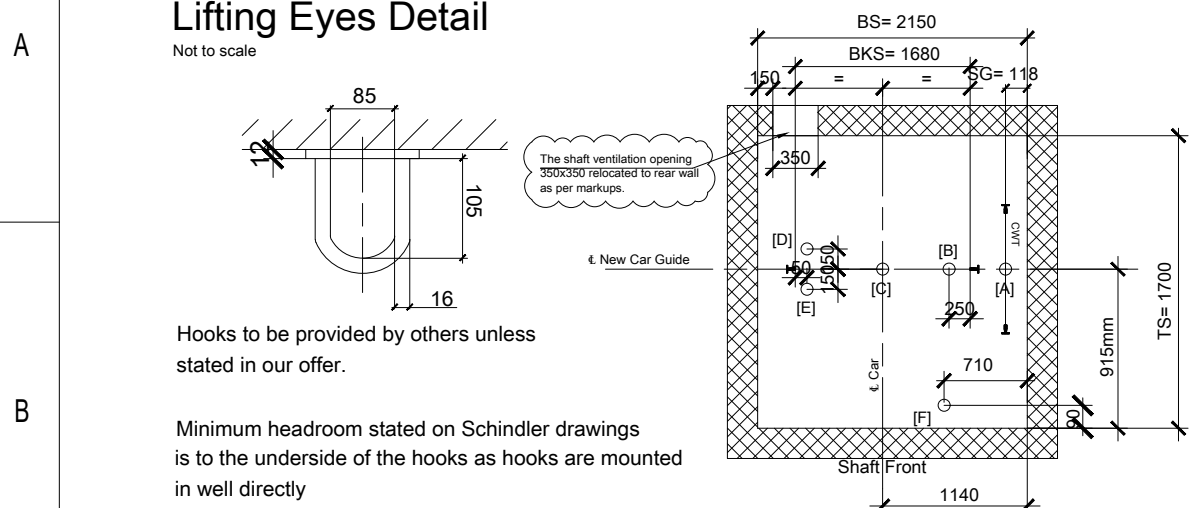





All dimensions and levels are from top of ramp (FFL+30mm/SSL+45mm) including HSK and HSG

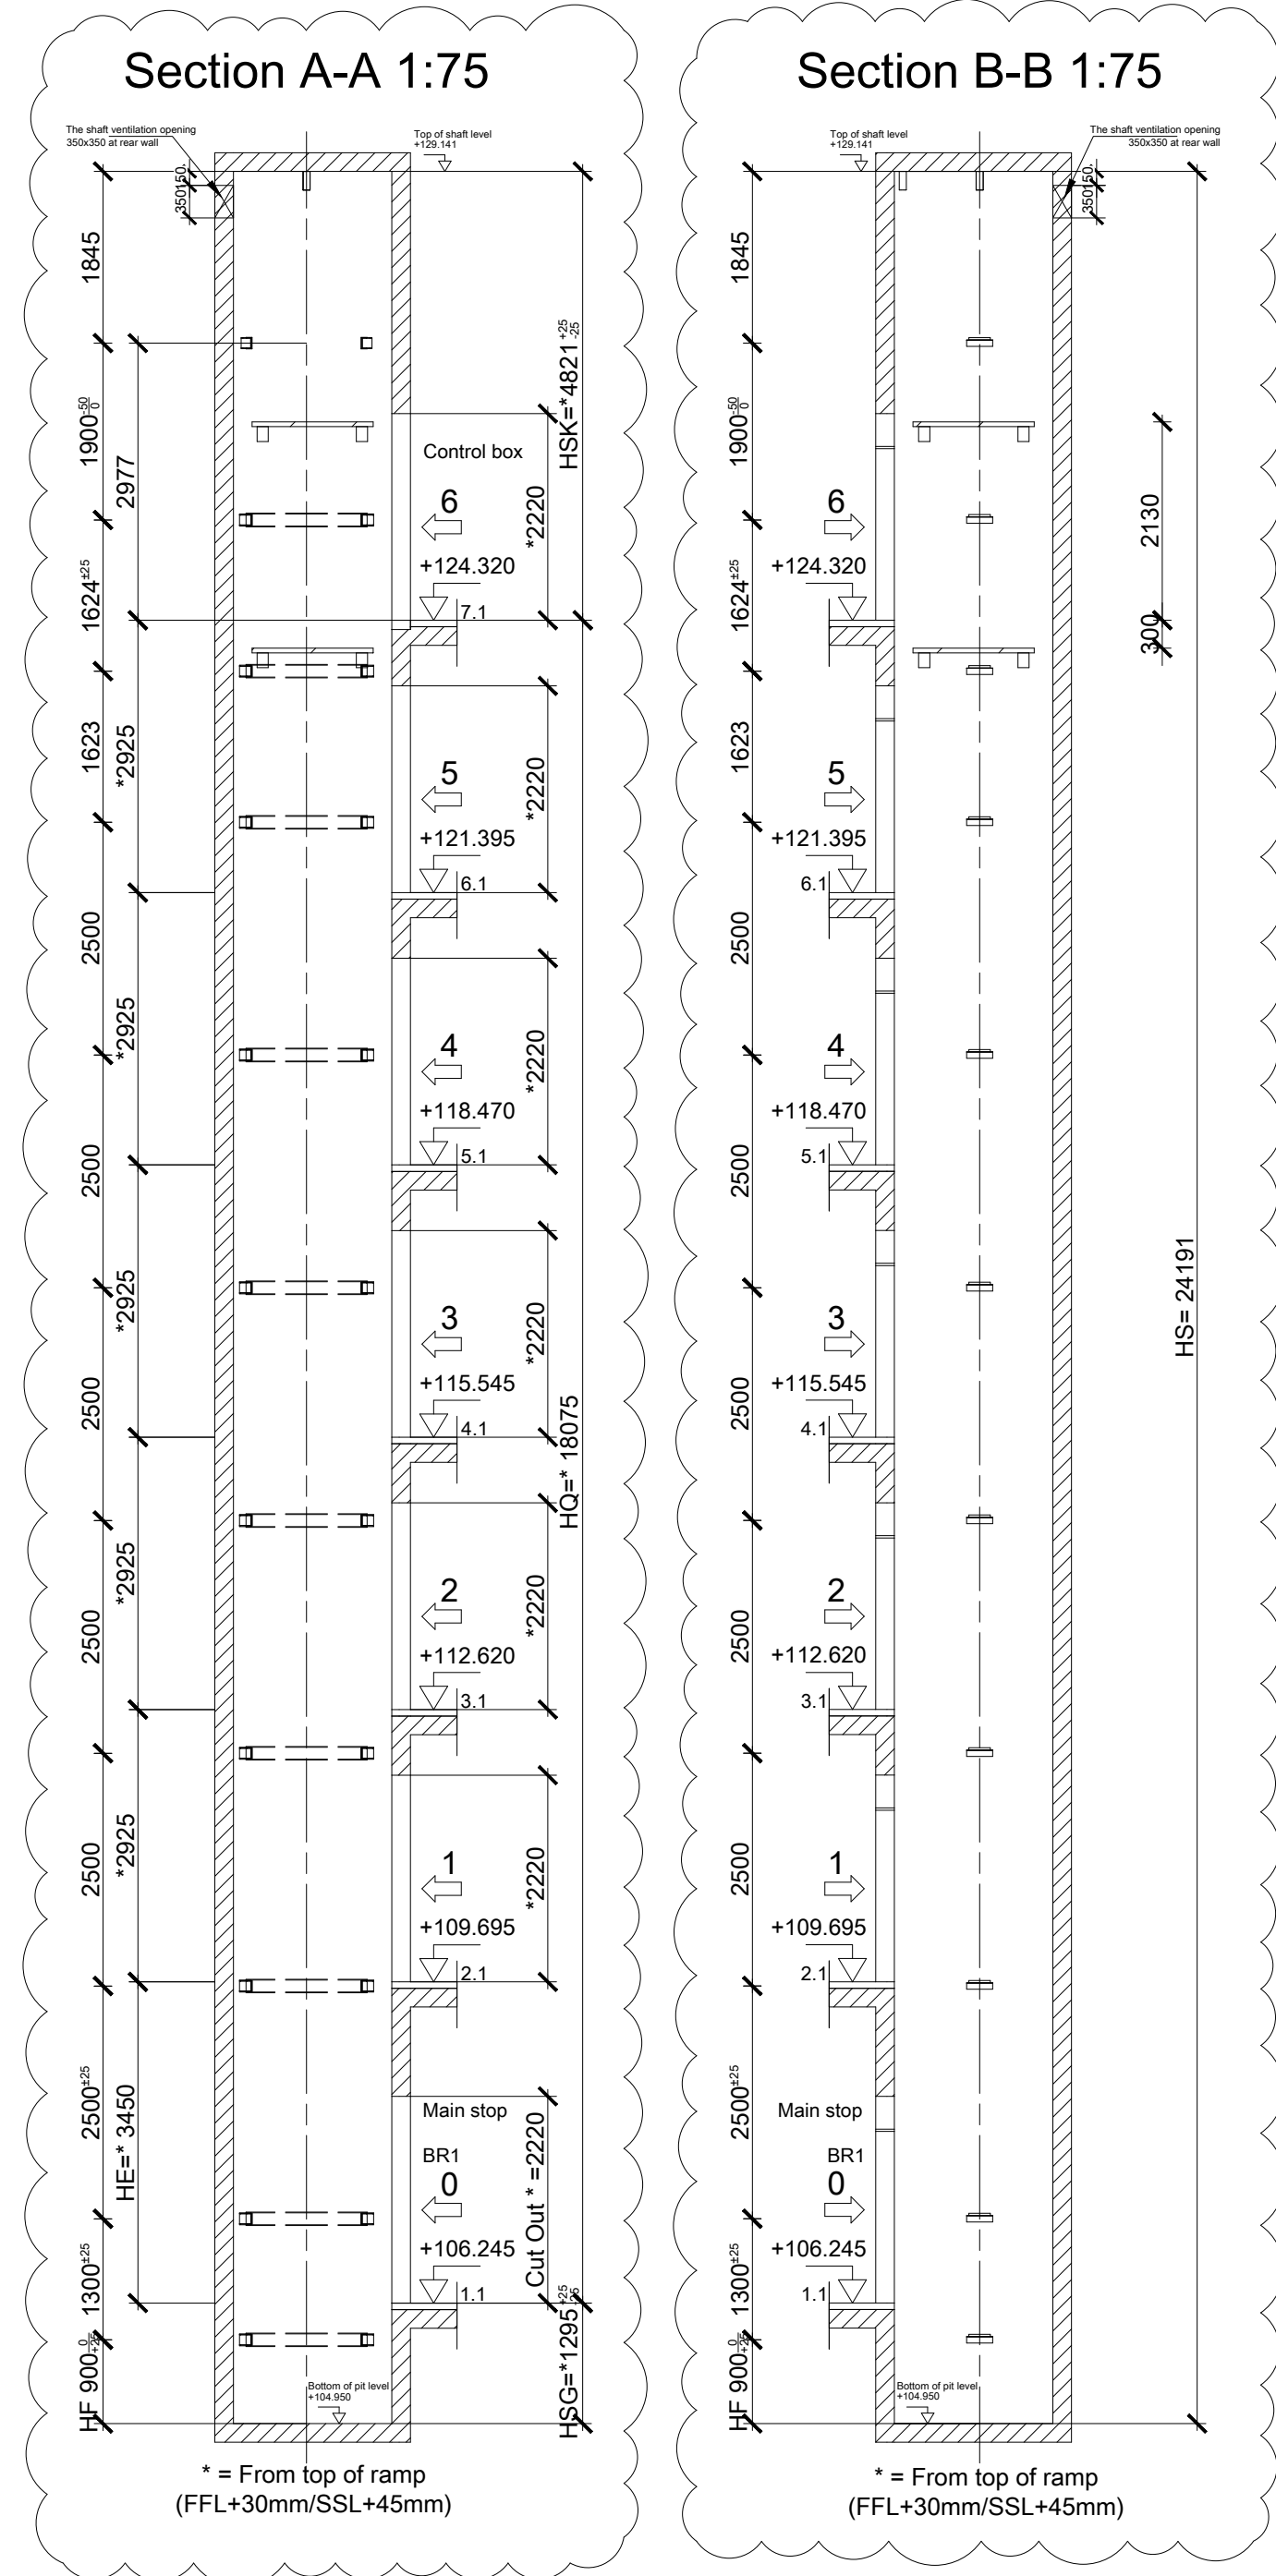

Hoistway loads							
F9 = 33961 N	F17 = -	F50x_T = 1208 N (Travel Section)		F50x_T = 664 N (Travel Section)			
F10 = 90378 N	F41 = -	F50x_PH = 2096 N (Pit and Head Section)		F50x_PH = 1103 N (Pit and Head Section)			
F11 = 34105 N	F42 = -	F50y_T = 105 Nm (Travel Section)		F50y_T = 105 Nm (Travel Section)			
F12 = 37134 N	F43 = -	M50z_T = 175 Nm (Pit and Head Section)		M50z_T = 175 Nm (Pit and Head Section)			
F13 = 26995 N	F44 = -	F51x_T = 1208 N (Travel Section)		F51x_T = 1208 N (Travel Section)			
F14 = 26995 N	F45 = -	F51y_T = 1133 N (Travel Section)		F51y_T = 1133 N (Travel Section)			
		F51x_PH = 2096 N (Pit and Head Section)		F51x_PH = 2096 N (Pit and Head Section)			
		F51y_PH = 1133 N (Pit and Head Section)		F51y_PH = 1133 N (Pit and Head Section)			
		M51z_T = 151 Nm (Travel Section)		M51z_T = 151 Nm (Travel Section)			
		M51z_PH = 317 Nm (Pit and Head Section)		M51z_PH = 317 Nm (Pit and Head Section)			
Bolt forces at bracket							
F54_max_dyn_s = -		F54_max_dyn_l = -		F54_max_dyn_s = -		F54_max_dyn_l = -	
F55_max_dyn_s = 1082 N		F55_max_dyn_l = 1869 N		F55_max_dyn_s = 1082 N		F55_max_dyn_l = 1869 N	
F56_max_dyn_s = -		F56_max_dyn_l = 690 N		F56_max_dyn_s = -		F56_max_dyn_l = 690 N	
F57_max_dyn_s = 359 N		F57_max_dyn_l = 690 N		F57_max_dyn_s = 359 N		F57_max_dyn_l = 690 N	
Load F11 & F12 only occur in case of operation of the safety gear.							
Loads F9 & F10 in case either car or counterweight lands on the buffers.							

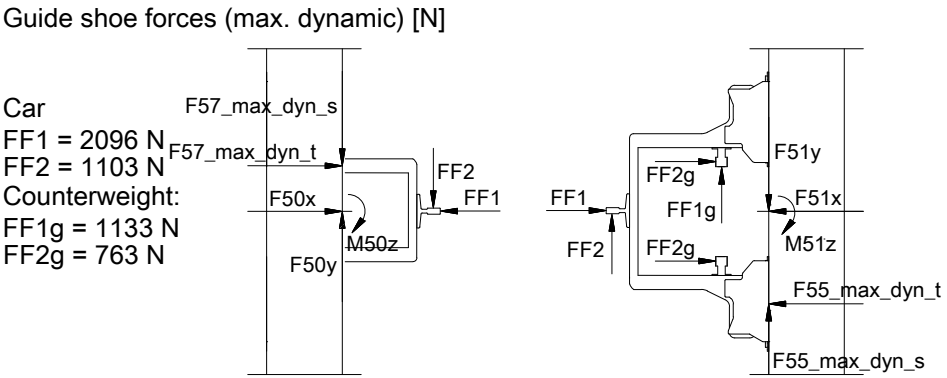

Refer to detail
SY1-CCL-ZZ-ZZ-SK-W-00001

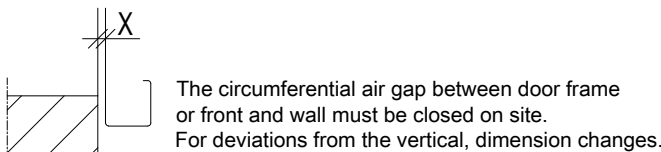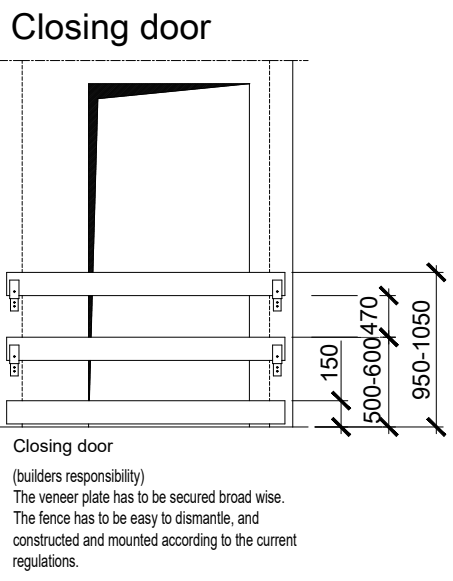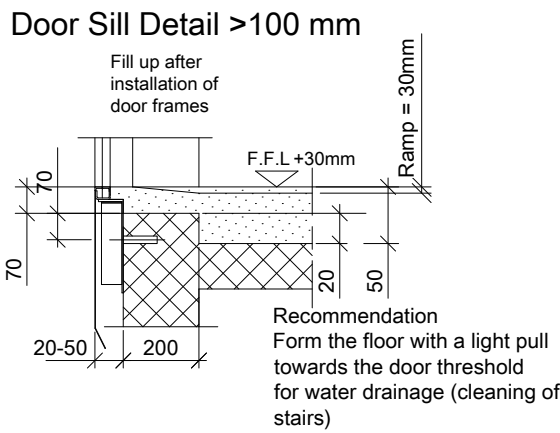

Revision	Modification	Modified by	Reviewed by	Date
P01	First Issue (CP 365)	ABOHAAN	HOOLEWI	28/08/2025
P02	Change counterweight position, ribs, Lift designation	BENAVUE	HOOLEWI	09/03/2026
C01	Issued to Construction	ABOHAAN	HOOLEWI	11/06/2026

Builder's work plan - Block F - Lift 2 FF				Product Line: Schindler 6000		
Building		Stoneyard, Birmingham - Phase 1				
Sales Unit Name		Block F - Lift 2 FF				
Address		High Street - B12 0NB Birmingham				
Client		Caddick Construction Limited - 31 Temple Street - B2 5DB Birmingham				
 Schindler	Schindler Ltd 409 Cashwood Lang Road Kourne Business Park B115 2HJ Edlestree		Further inquiries concerning this plan on Keith Docherty Tel:			
			Drawn	ABOCHAAN	28/08/2025	Page
			Released	KEITH	28/08/2025	1/6
	Contact: Keith Docherty		Comm. No. UKC0011915015			
		Plan No. SY1-SCH-BF-ZZ-DR-X-01100				
		C0				